




BFS Operations LLC
3980 Matthews Indian Trail Rd
Indian Trail NC 28106
Phone 704-821-8641
Email vinny.spaulding@bldr.com

GLASS ORDER

Printed On: 6/3/2026

Supplier: Internal - BFS
Delivery Date: 6/9/2026
Address: 3980 Matthews Indian Trail Rd
Indian Trail NC 28106

Project Name: 87829468 CORDERA 6
Project #: NIBLOCK
Location: MASTER

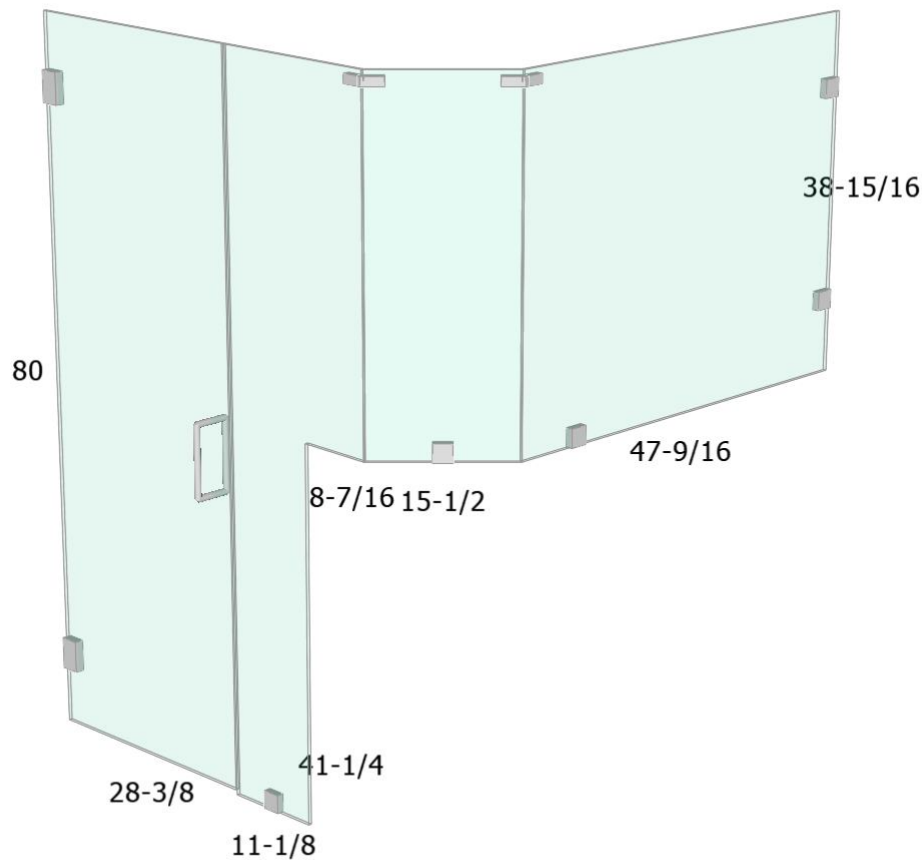

Total of 4 Panel(s) in this Order **Total Area: 43.57sq ft** **Total Weight: 214.37lb**
Measurements are in inches

3/8" Clear Tempered

4 ea As per attached drawings

1 ea

3/8" Clear Tempered

28-1/8" x 79-1/2" (76.4lb)

Flat Polish 2 Long 2 Short As Shown

Tempered logo in Bottom Left Corner


Measurements are in inches

Project #: NIBLOCK

Location: MASTER

Marks: P1

Raked Edge

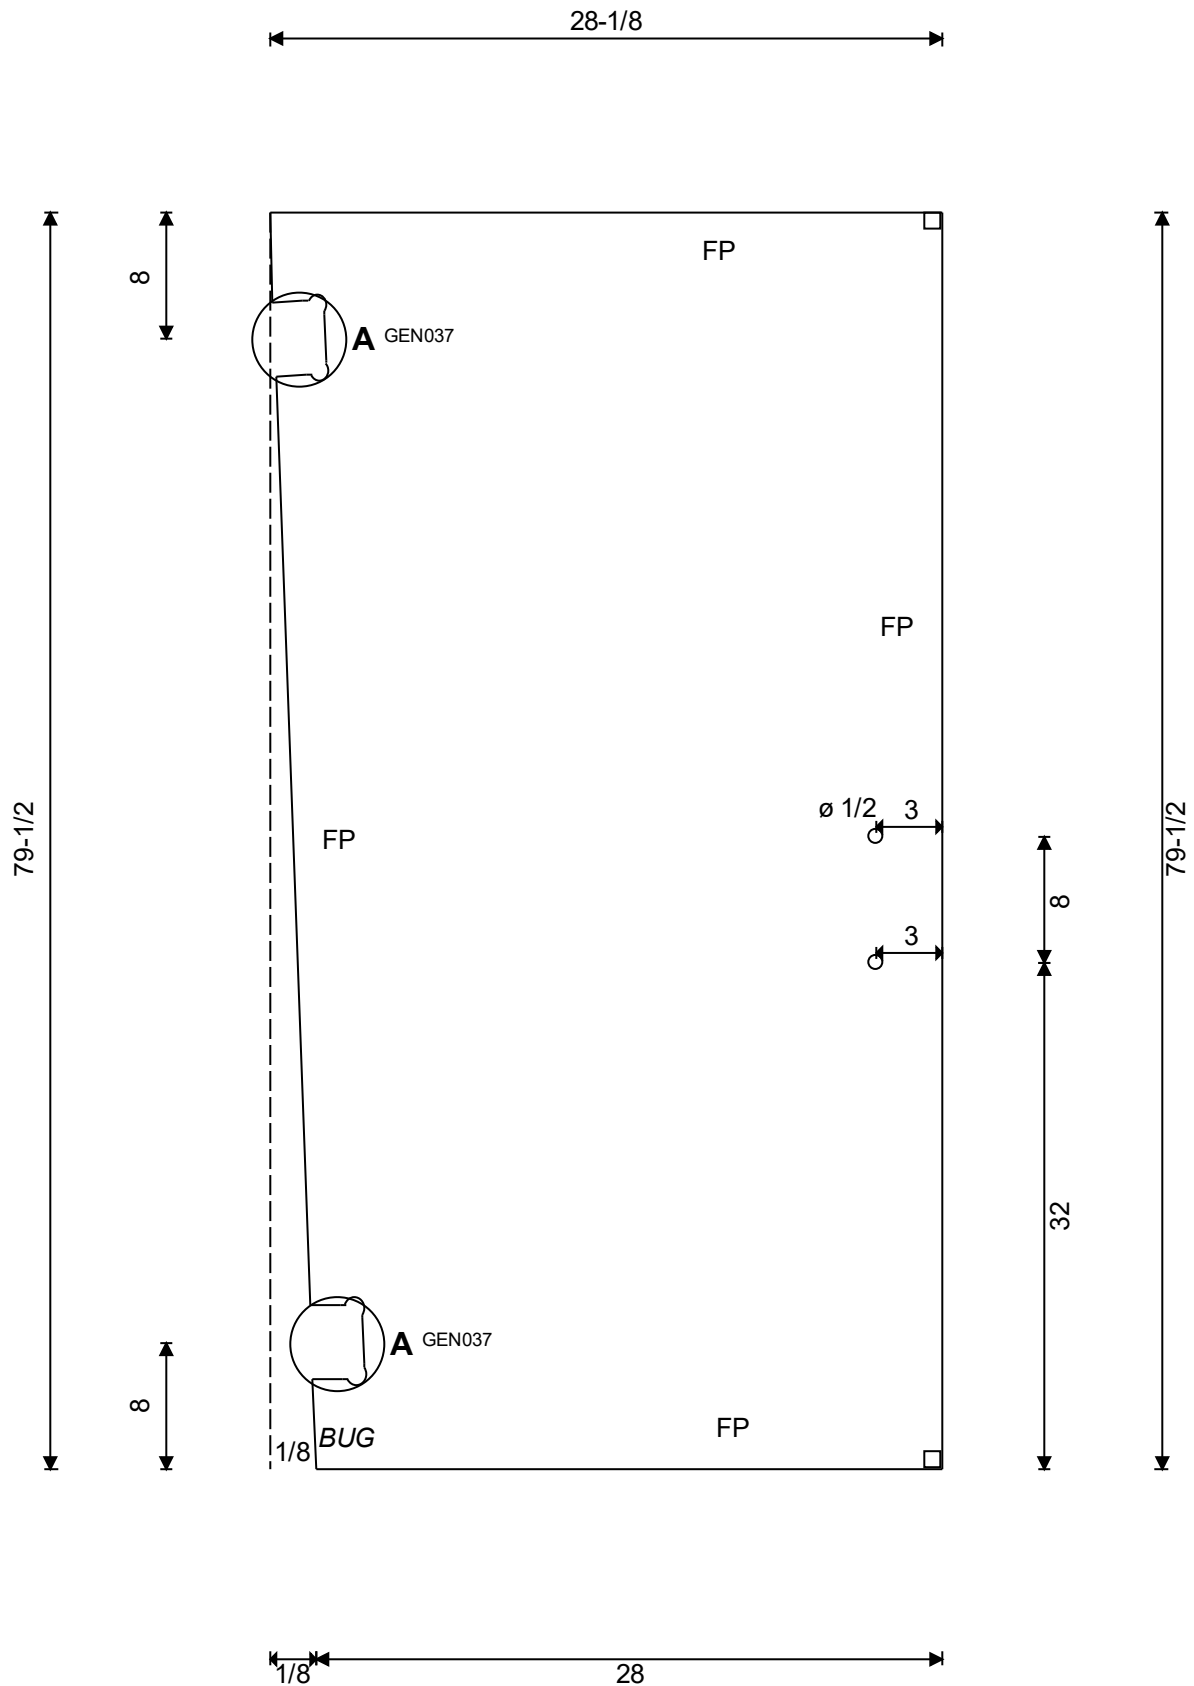

1 ea

3/8" Clear Tempered

19-3/4" x 80" (54lb)

Flat Polish 1 Long 2 Short As Shown

22.5° Polished Back Miter 1 Long As Shown


Tempered logo in Bottom Right Corner

Measurements are in inches

Project #: NIBLOCK

Location: MASTER

Marks: P2

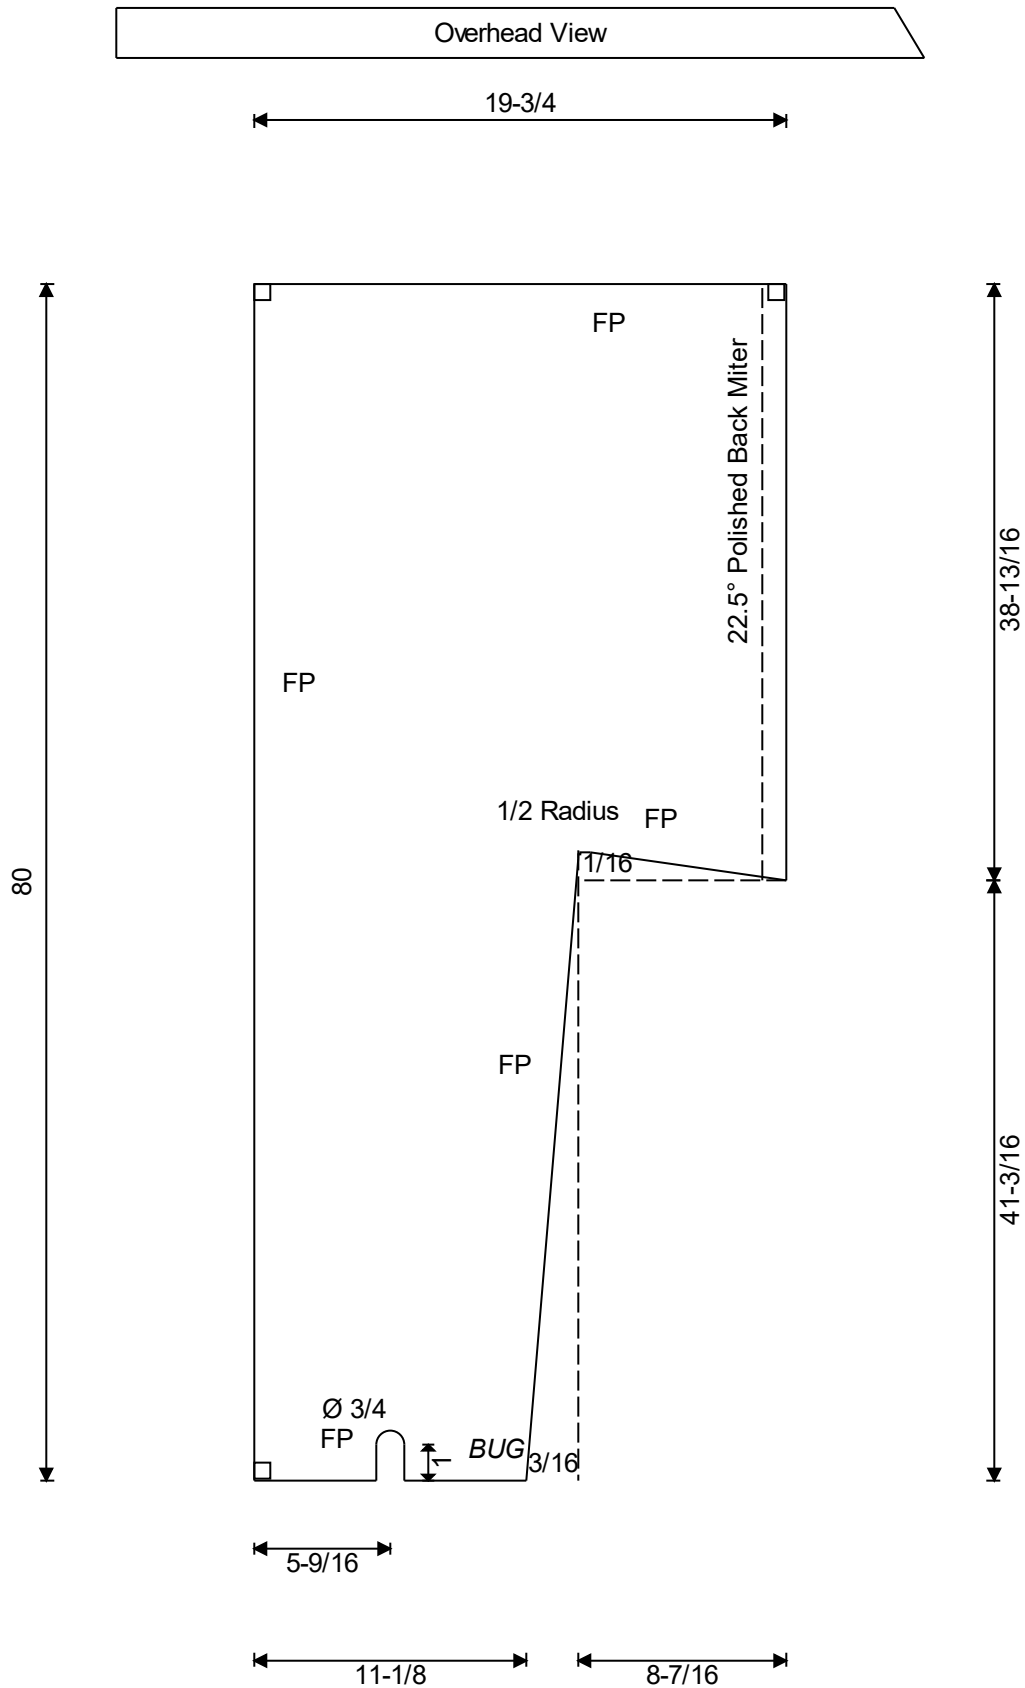

1 ea

3/8" Clear Tempered

15-1/2" x 38-13/16" (20.6lb)

22.5° Polished Back Miter 2 Long As Shown

Flat Polish 2 Short As Shown


Tempered logo in Bottom Right Corner

Measurements are in inches

Project #: NIBLOCK

Location: MASTER

Marks: P3

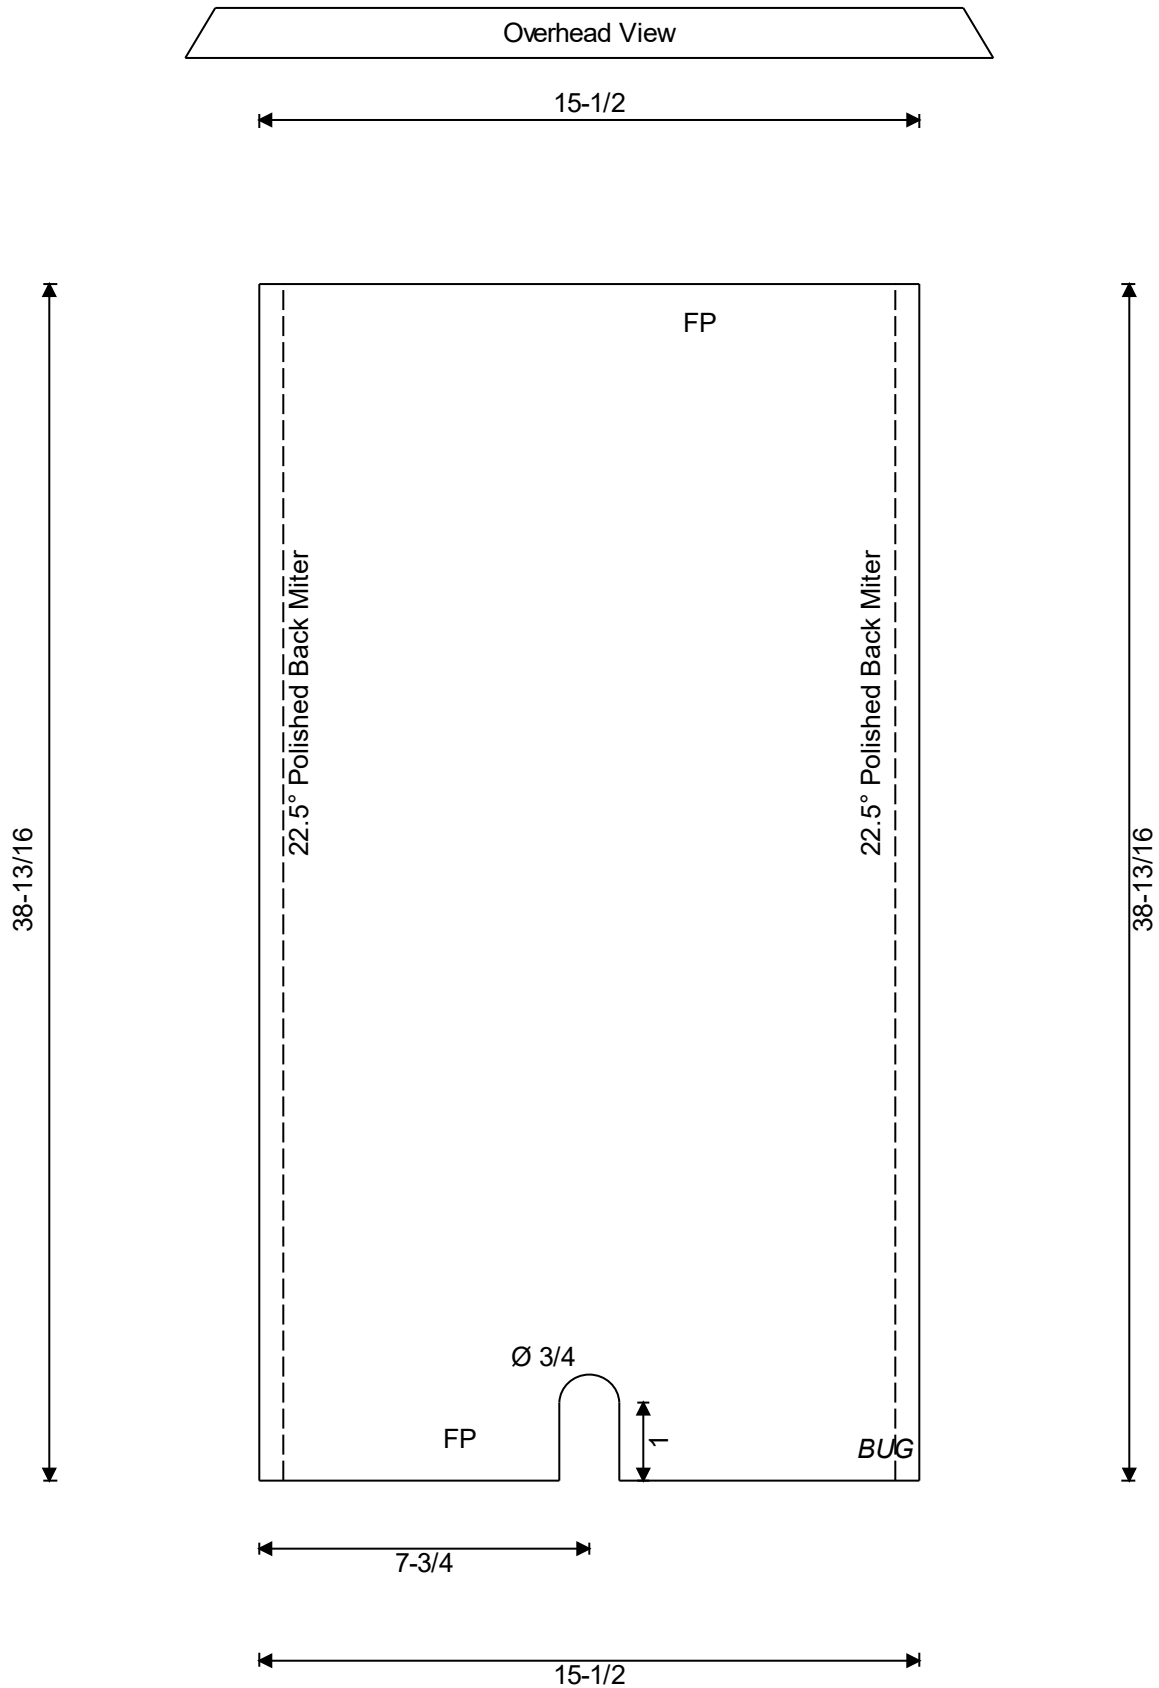

1 ea

3/8" Clear Tempered



47-11/16" x 38-15/16" (63.4lb)
22.5° Polished Back Miter 1 Short As Shown
Flat Polish 2 Long 1 Short As Shown
Tempered logo in Bottom Right Corner
Measurements are in inches

Project #: NIBLOCK


Location: MASTER

Marks: P4

Irregular Shape

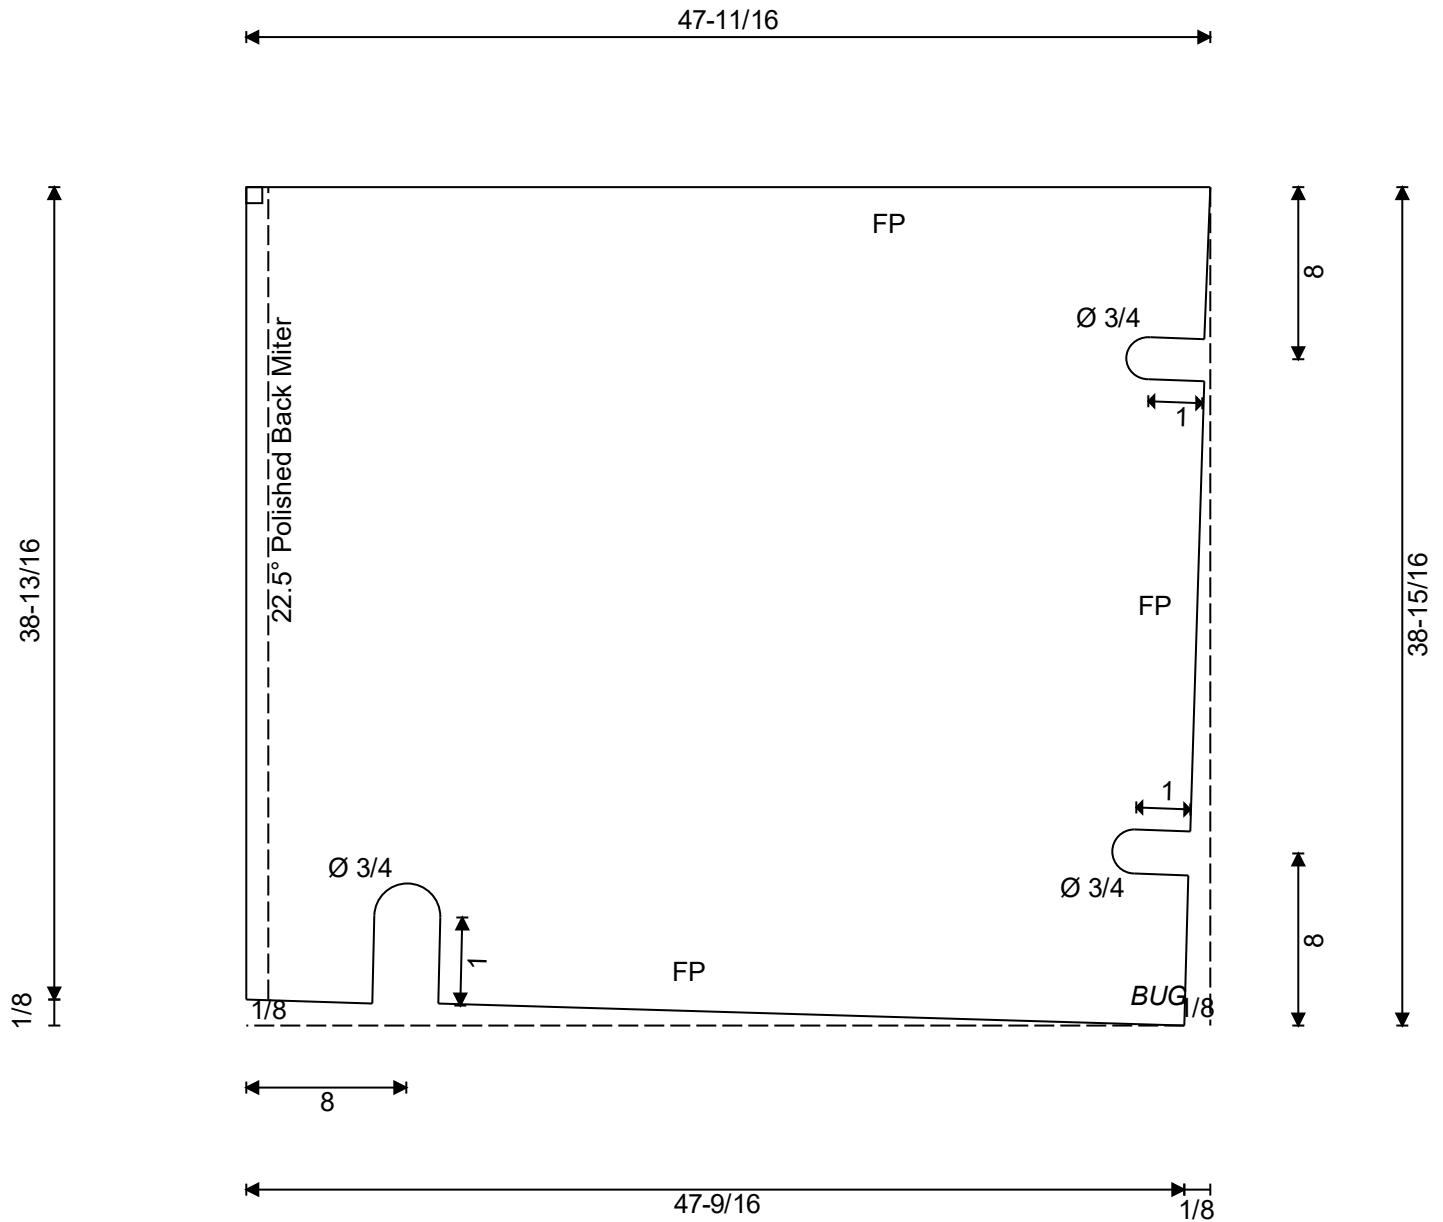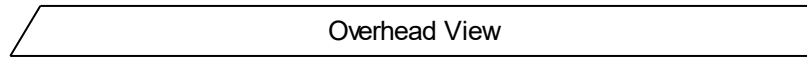

Template A: GEN037

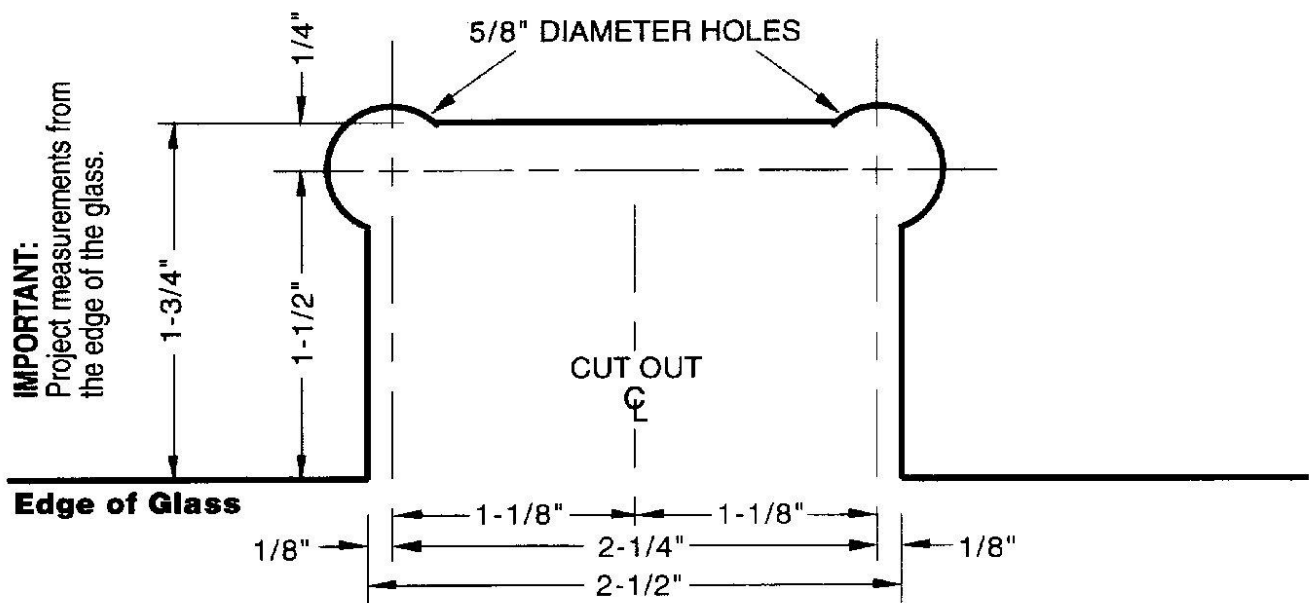

Drawing is not to Scale