




BFS Operations LLC
3980 Matthews Indian Trail Rd
Indian Trail NC 28106
Phone 704-821-8641
Email brandon.m.smith@bldr.com

GLASS ORDER

Printed On: 6/4/2026

Supplier: Internal - BFS
Delivery Date: 6/10/2026
Address: 3980 Matthews Indian Trail Rd
Indian Trail NC 28106

Project Name: 88304166 775 MENDENHALL
Project #: PARAGON
Location: MASTER

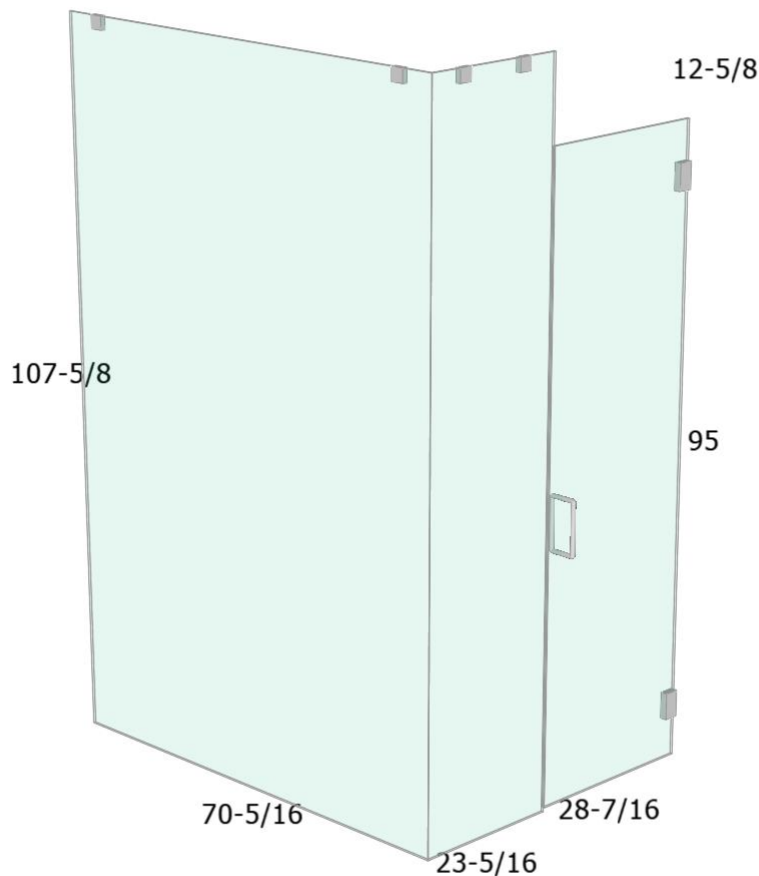

Total of 3 Panel(s) in this Order **Total Area: 89.05sq ft** **Total Weight: 438.13lb**
Measurements are in inches

3/8" Clear Tempered

3 ea As per attached drawings

1 ea

3/8" Clear Tempered

71-1/4" x 107-5/8" (262lb)

Flat Polish 1 Long 2 Short As Shown

45° Polished Back Miter 1 Long As Shown

Tempered logo in Bottom Left Corner


Measurements are in inches

Project #: PARAGON

Location: MASTER

Marks: P1

Raked Edge

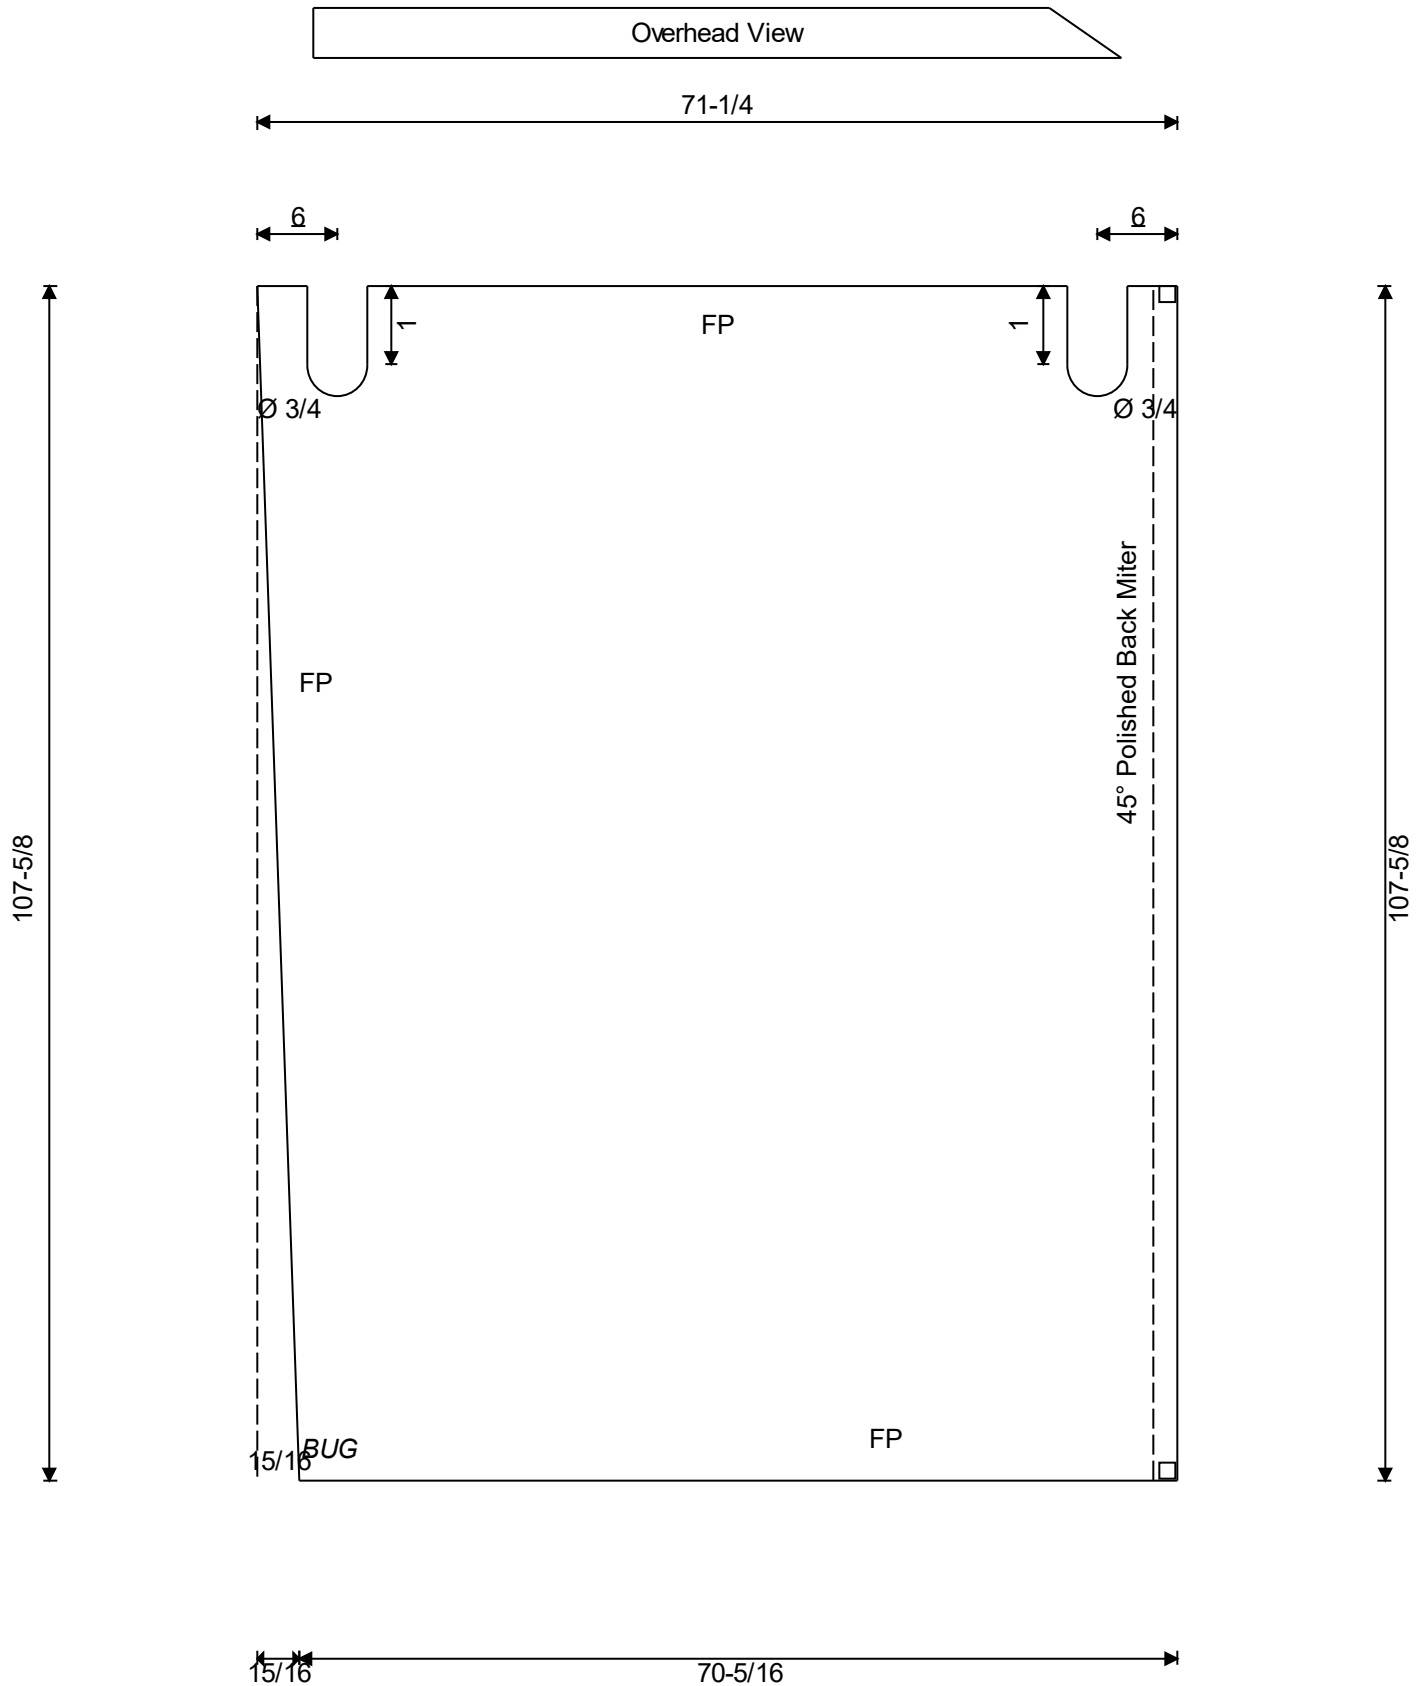

1 ea

3/8" Clear Tempered

23-5/16" x 107-5/8" (85.7lb)

45° Polished Back Miter 1 Long As Shown

Flat Polish 1 Long 2 Short As Shown


Tempered logo in Bottom Left Corner

Measurements are in inches

Project #: PARAGON

Location: MASTER

Marks: P2

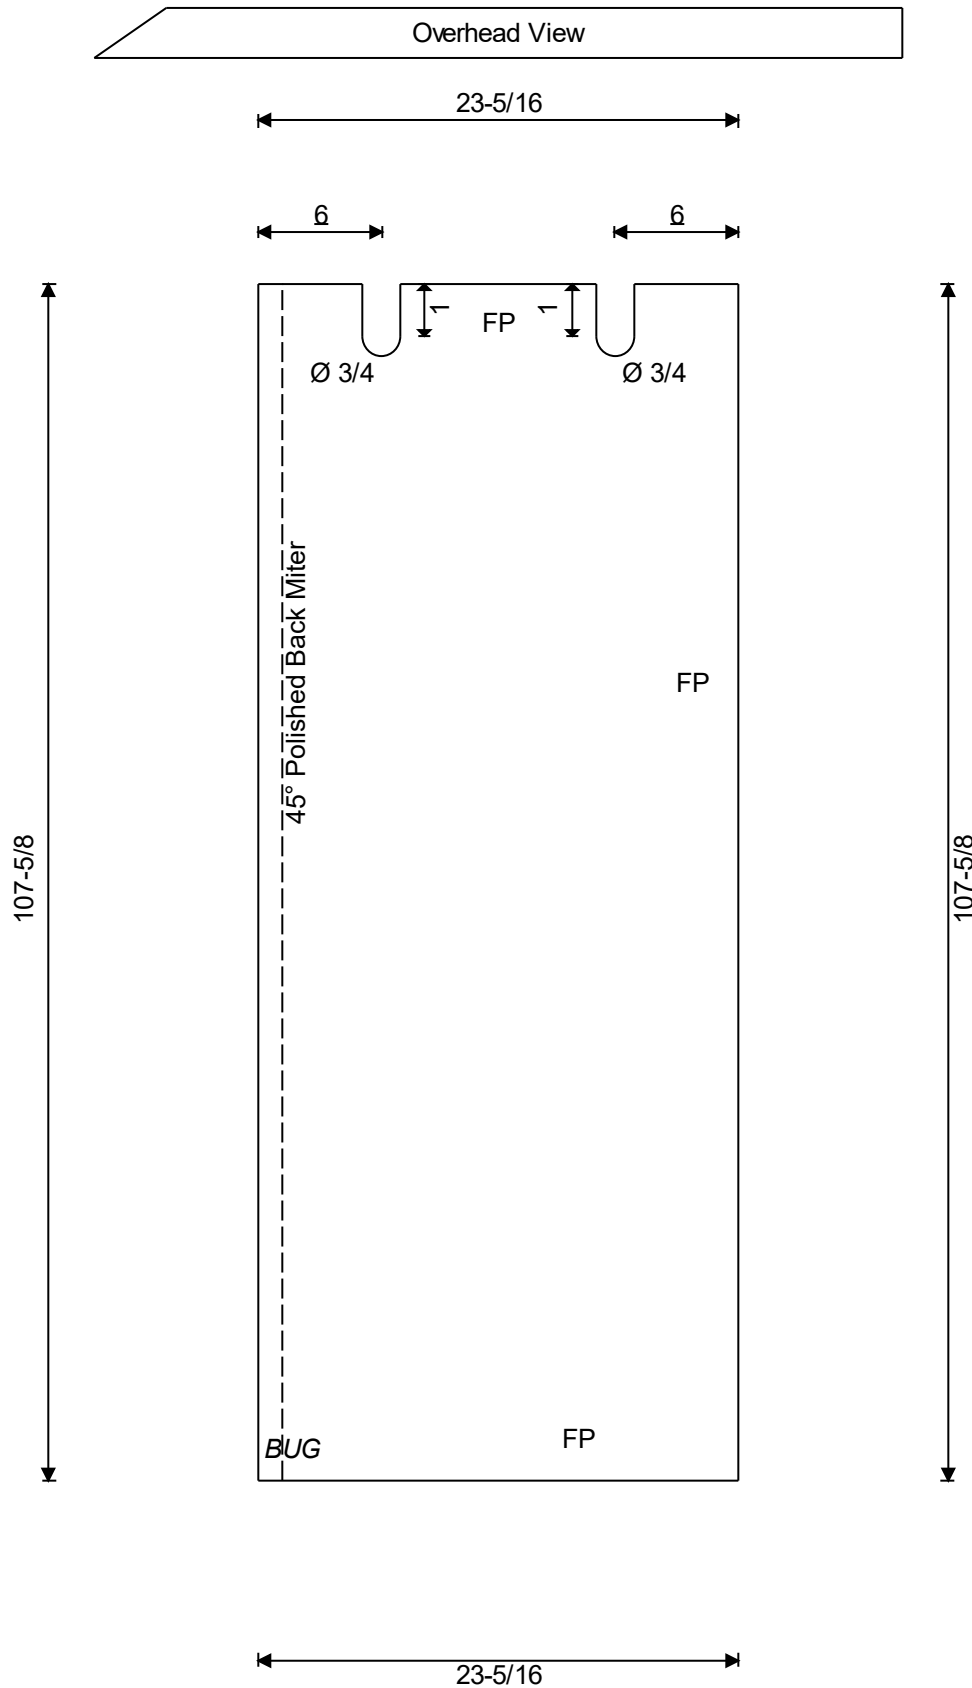

3/8" Clear Tempered

28" x 94-1/2" (90.4lb)


Flat Polish 2 Long 2 Short As Shown
Tempered logo in Bottom Right Corner
Measurements are in inches

Project #: PARAGON

Location: MASTER

Marks: P3

Raked Edge

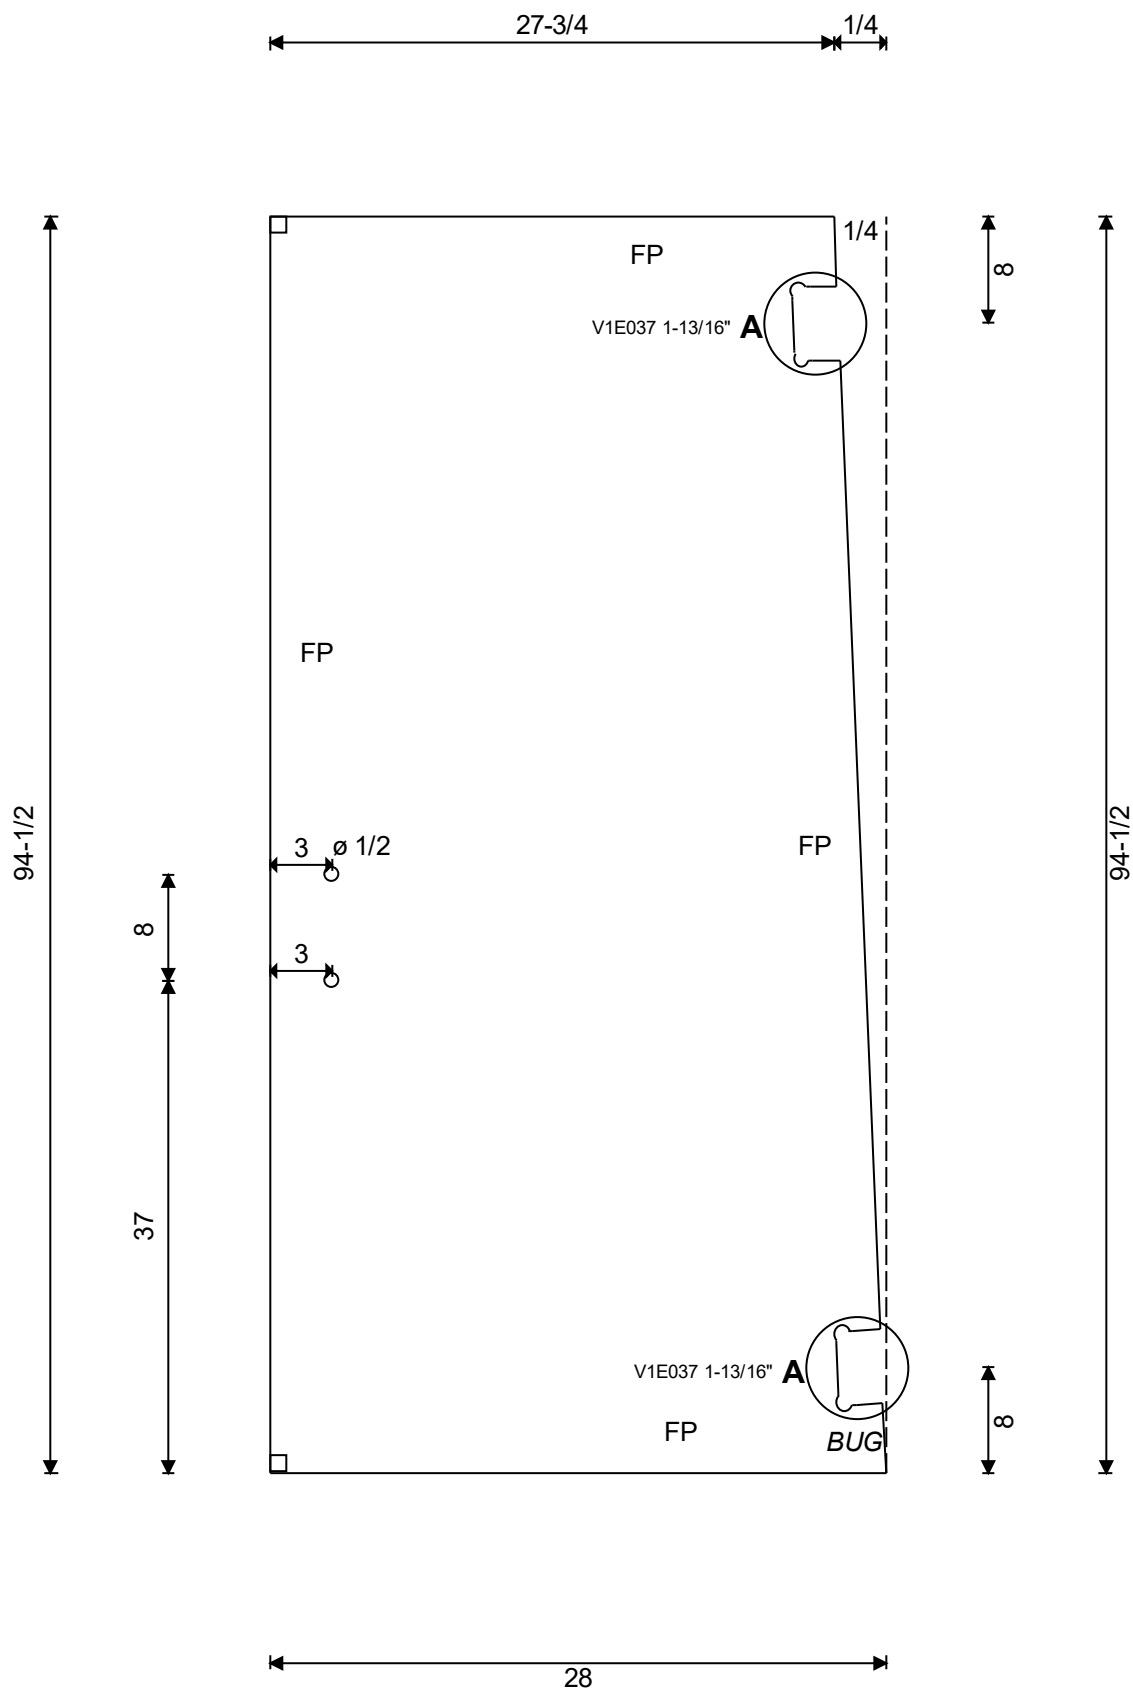

Template A: V1E037 1-13/16"

