




BFS Operations LLC
3980 Matthews Indian Trail Rd
Indian Trail NC 28106
Phone 704-821-8641
Email vinny.spaulding@bldr.com

GLASS ORDER

Printed On: 6/8/2026

Supplier: Internal - BFS
Delivery Date: 6/12/2026
Address: 3980 Matthews Indian Trail Rd
Indian Trail NC 28106

Project Name: 88340724 1592 CALIFORNIA
Project #: TERRAIN
Location: MASTER

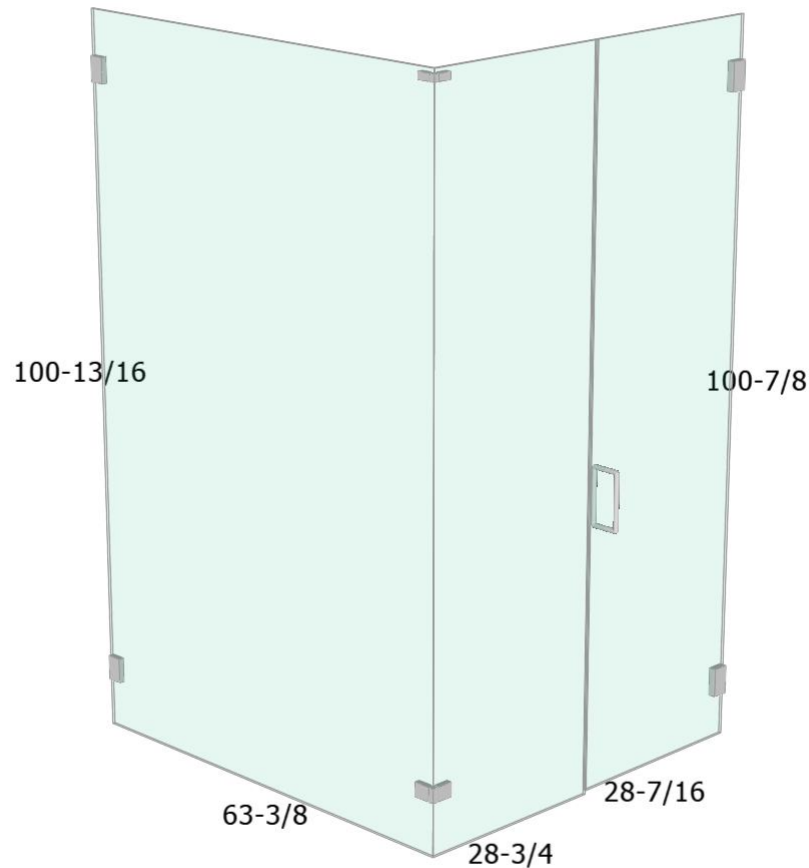

Total of 3 Panel(s) in this Order **Total Area: 84.28sq ft** **Total Weight: 414.64lb**
Measurements are in inches

3/8" Clear Tempered

3 ea As per attached drawings

1 ea

3/8" Clear Tempered

63-3/8" x 100-7/8" (218.4lb)

Flat Polish 1 Long 2 Short As Shown

45° Polished Back Miter 1 Long As Shown

Tempered logo in Bottom Left Corner


Measurements are in inches

Project #: TERRAIN

Location: MASTER

Marks: P1

Raked Edge

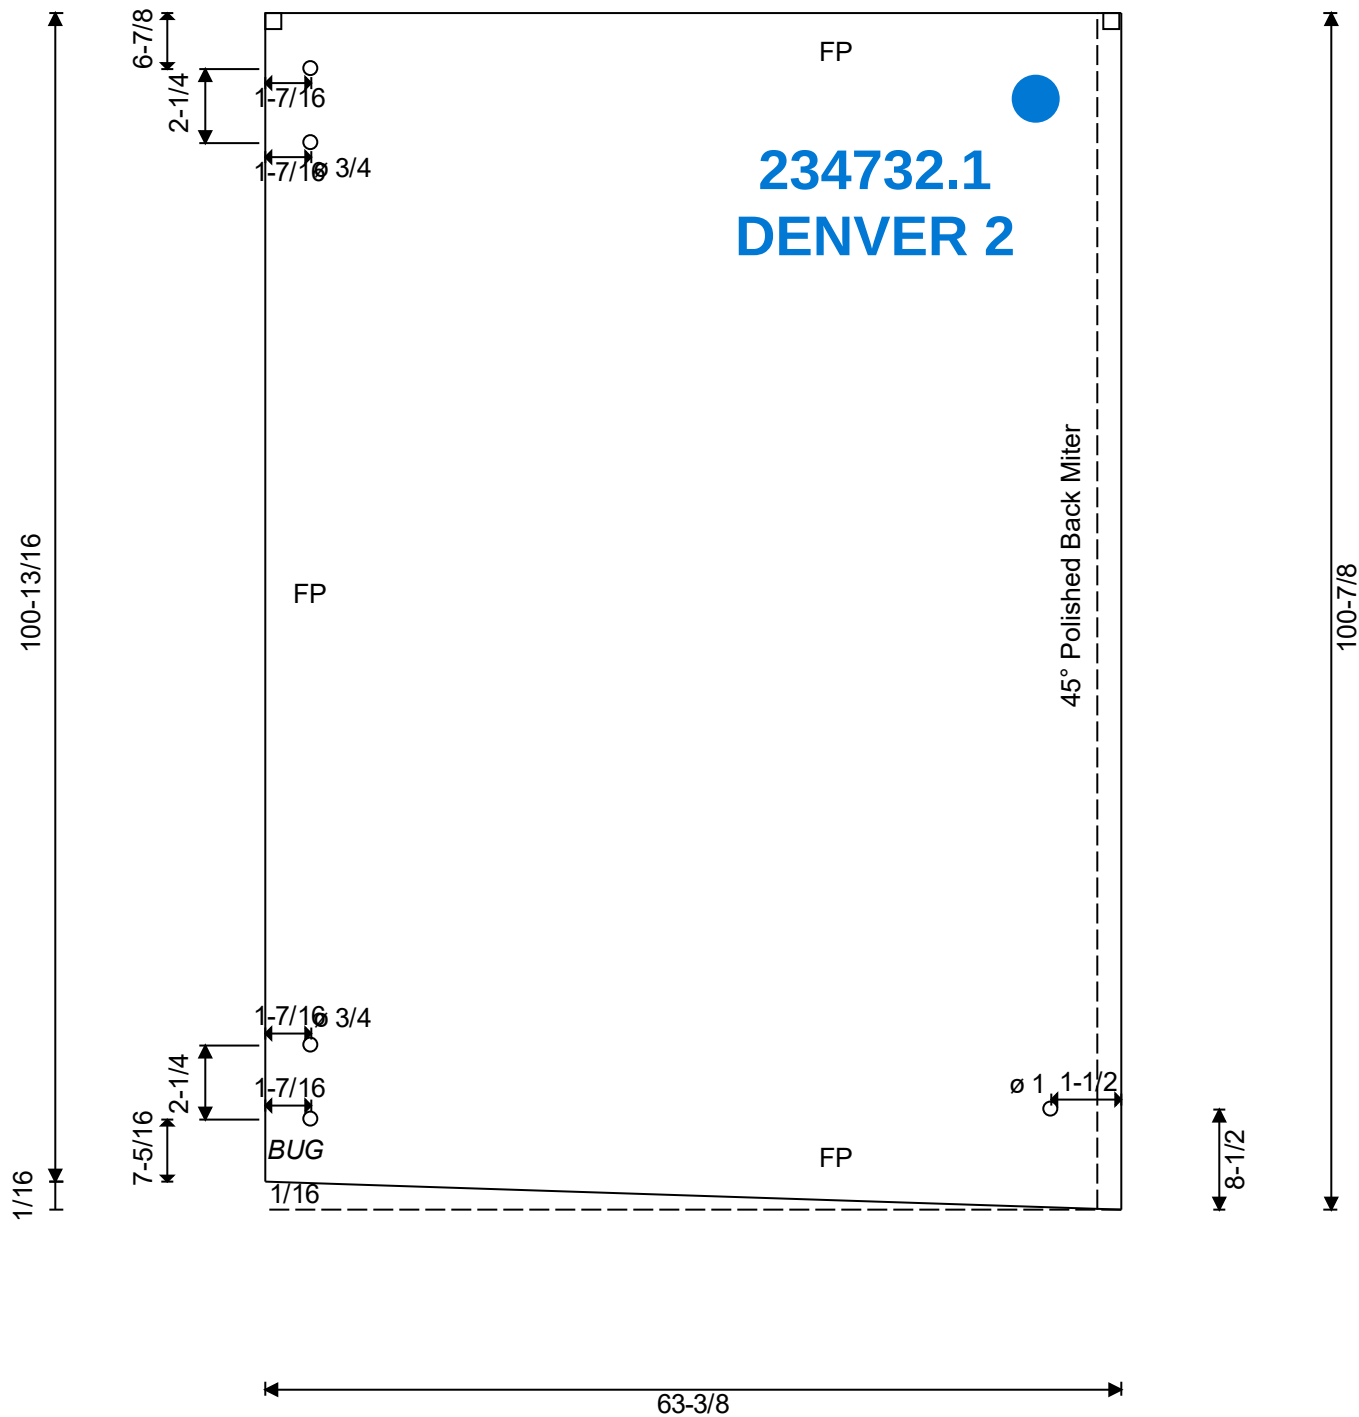

1 ea

3/8" Clear Tempered


28-3/4" x 101" (99.2lb)
45° Polished Back Miter 1 Long As Shown
Flat Polish 1 Long 2 Short As Shown
Tempered logo in Bottom Left Corner
Measurements are in inches

Project #: TERRAIN

Location: MASTER

Marks: P2

Raked Edge

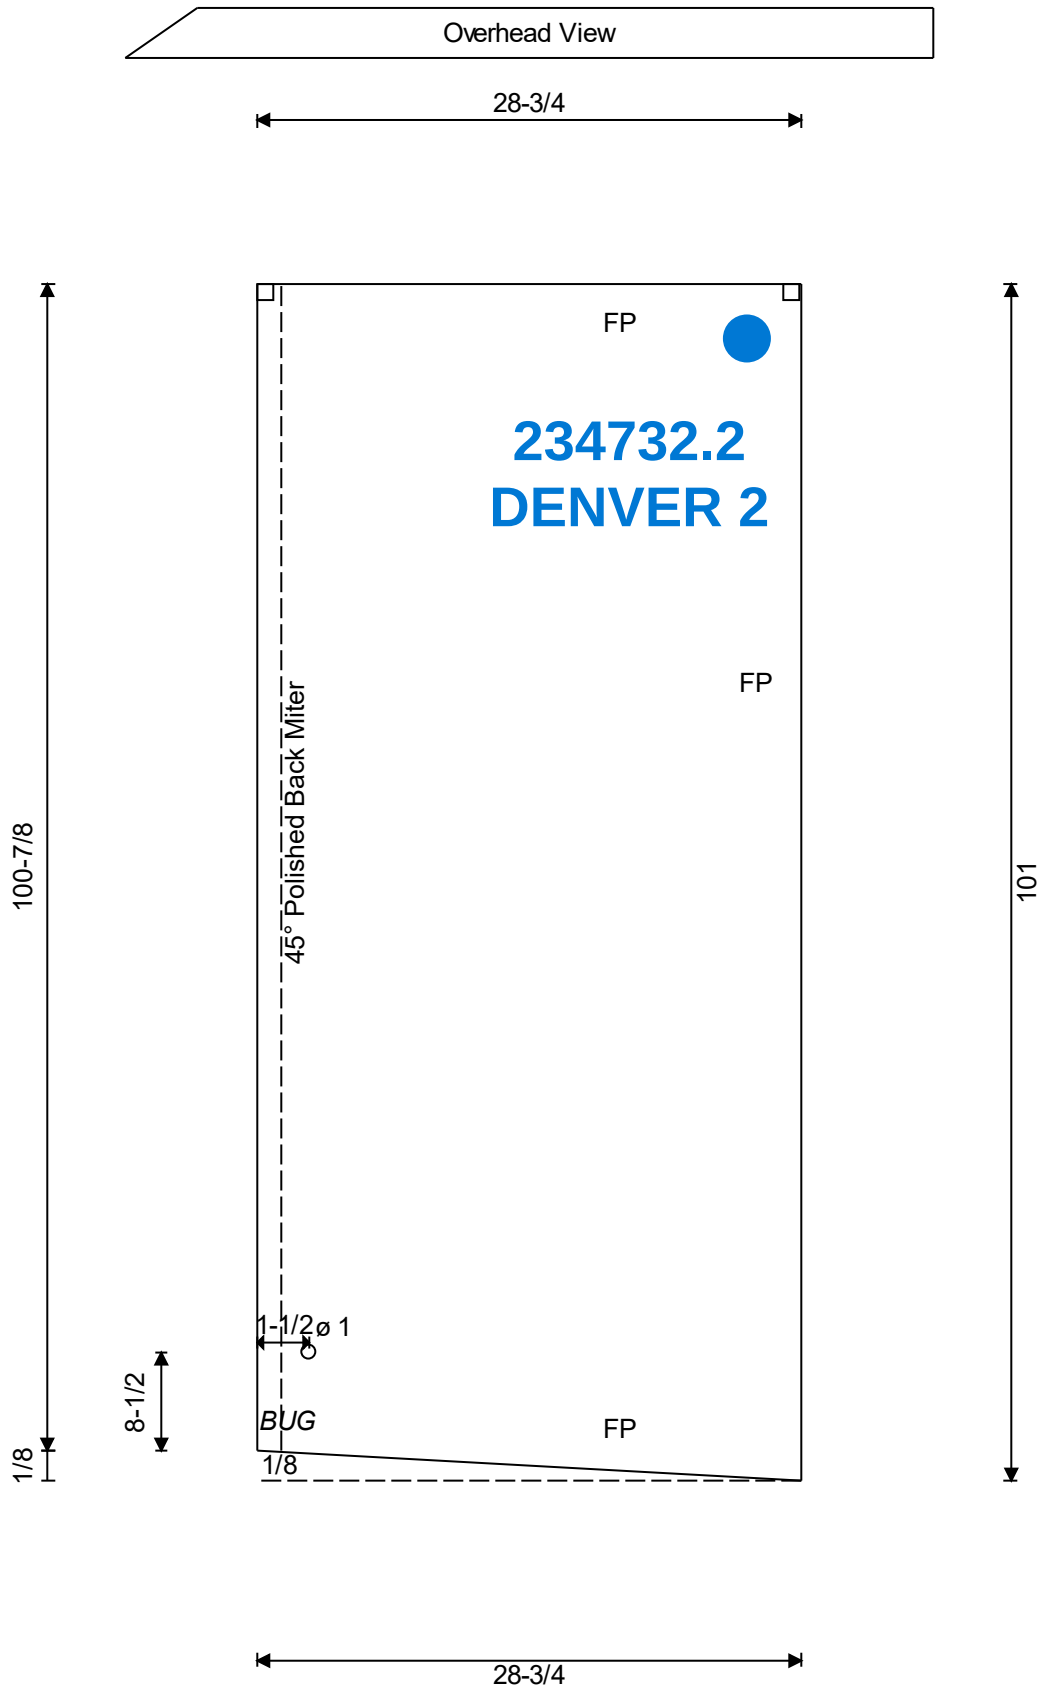

1 ea

3/8" Clear Tempered

28-1/4" x 100-1/2" (97lb)

Flat Polish 2 Long 2 Short As Shown

Tempered logo in Bottom Right Corner


Measurements are in inches

Project #: TERRAIN

Location: MASTER

Marks: P3

Irregular Shape

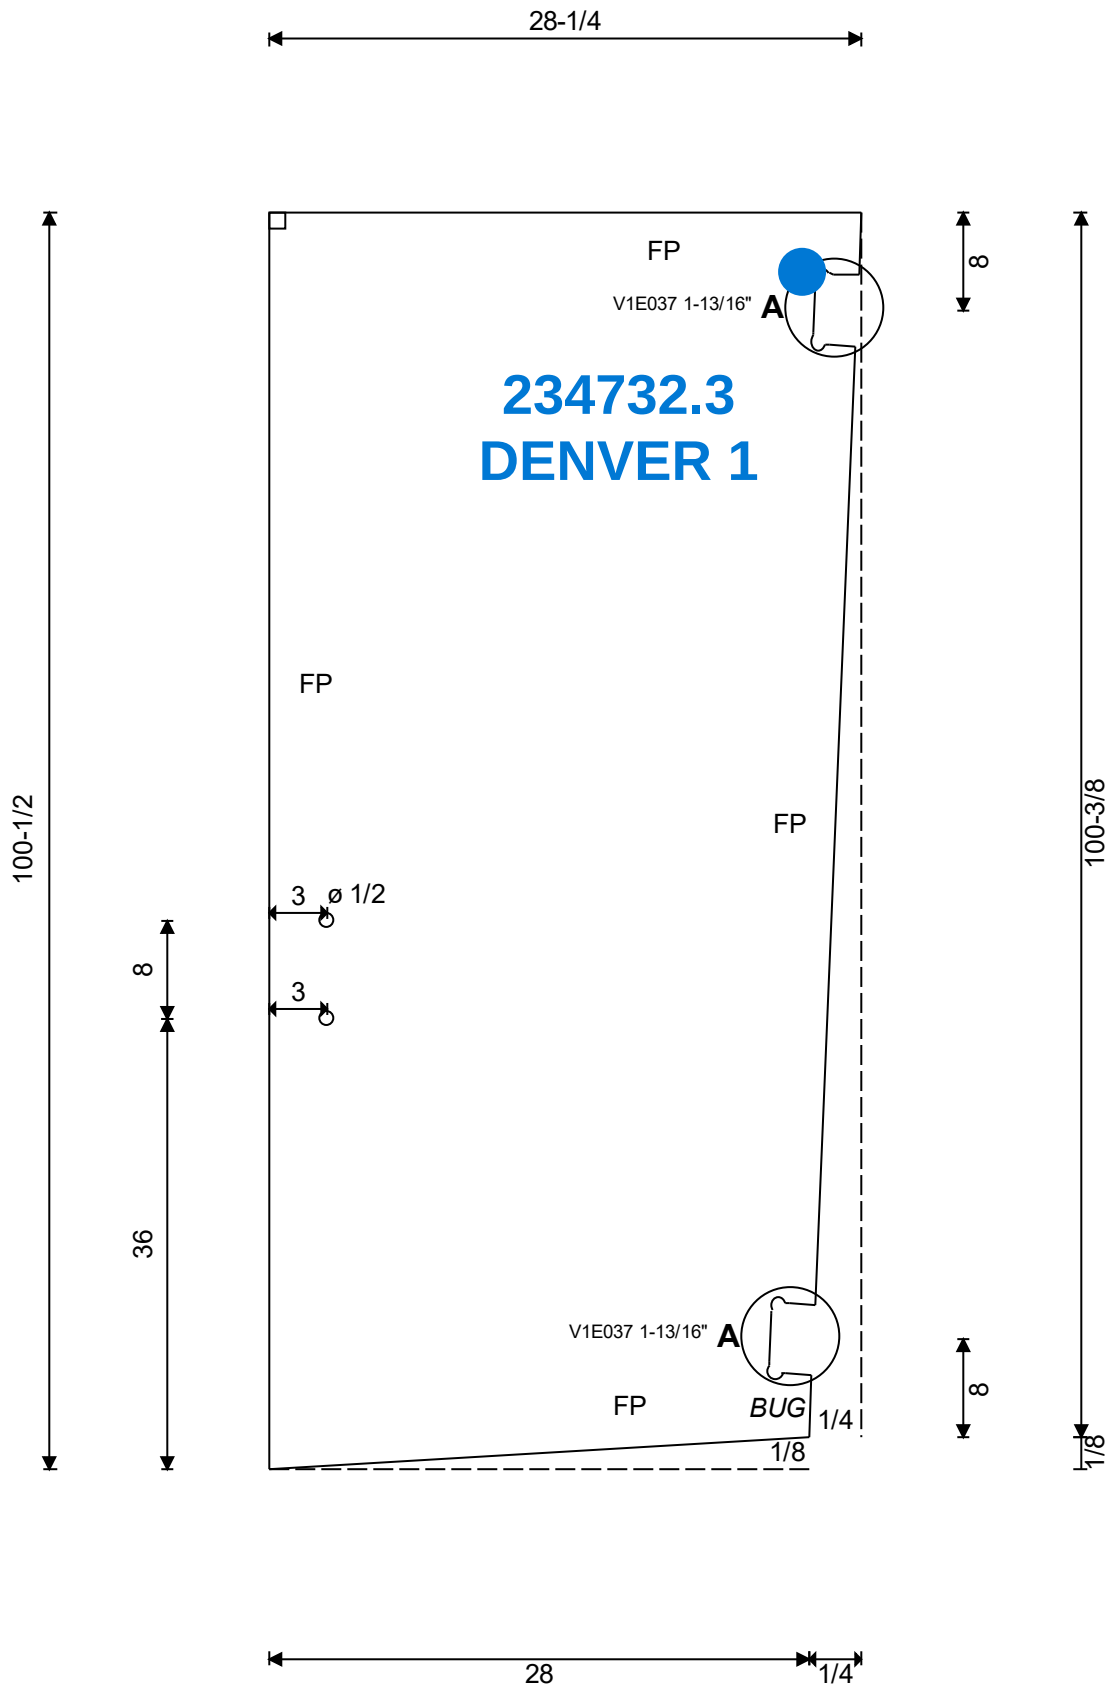

Template A: V1E037 1-13/16"

